

PERMANENT EASEMENT
ACROSS PARCEL NO. 583-25-002
PART OF ORIGINAL BRECKSVILLE
TOWNSHIP LOT NO. 25
CITY OF BROADVIEW HEIGHTS,
COUNTY OF CUYAHOGA,
STATE OF OHIO

ABBREVIATIONS

AFN AUTOMATIC FILE NUMBER
CCMR CUYAHOGA COUNTY MAP RECORDS
POB POINT OF BEGINNING

CURVE TABLE					
CURVE	RADIUS	LENGTH	DELTA	BEARING	CHORD
C1	1115.92'	223.33'	011°28'00"	N35°12'16"W	222.96'
C2	705.00'	572.34'	046°30'53"	N42°07'41"W	556.76'




1" = 300'



Trevor A. Bixler 5-22-19

TREVOR A. BIXLER
PROFESSIONAL SURVEYOR, OHIO NO. 7730

R:\17000\17185-STAN\CIVIL 3D 2014\CURRENT DRAWINGS\BASE DRAWINGS\DWG\17185_Harris_Road_Ease.dwg 6/12/2019

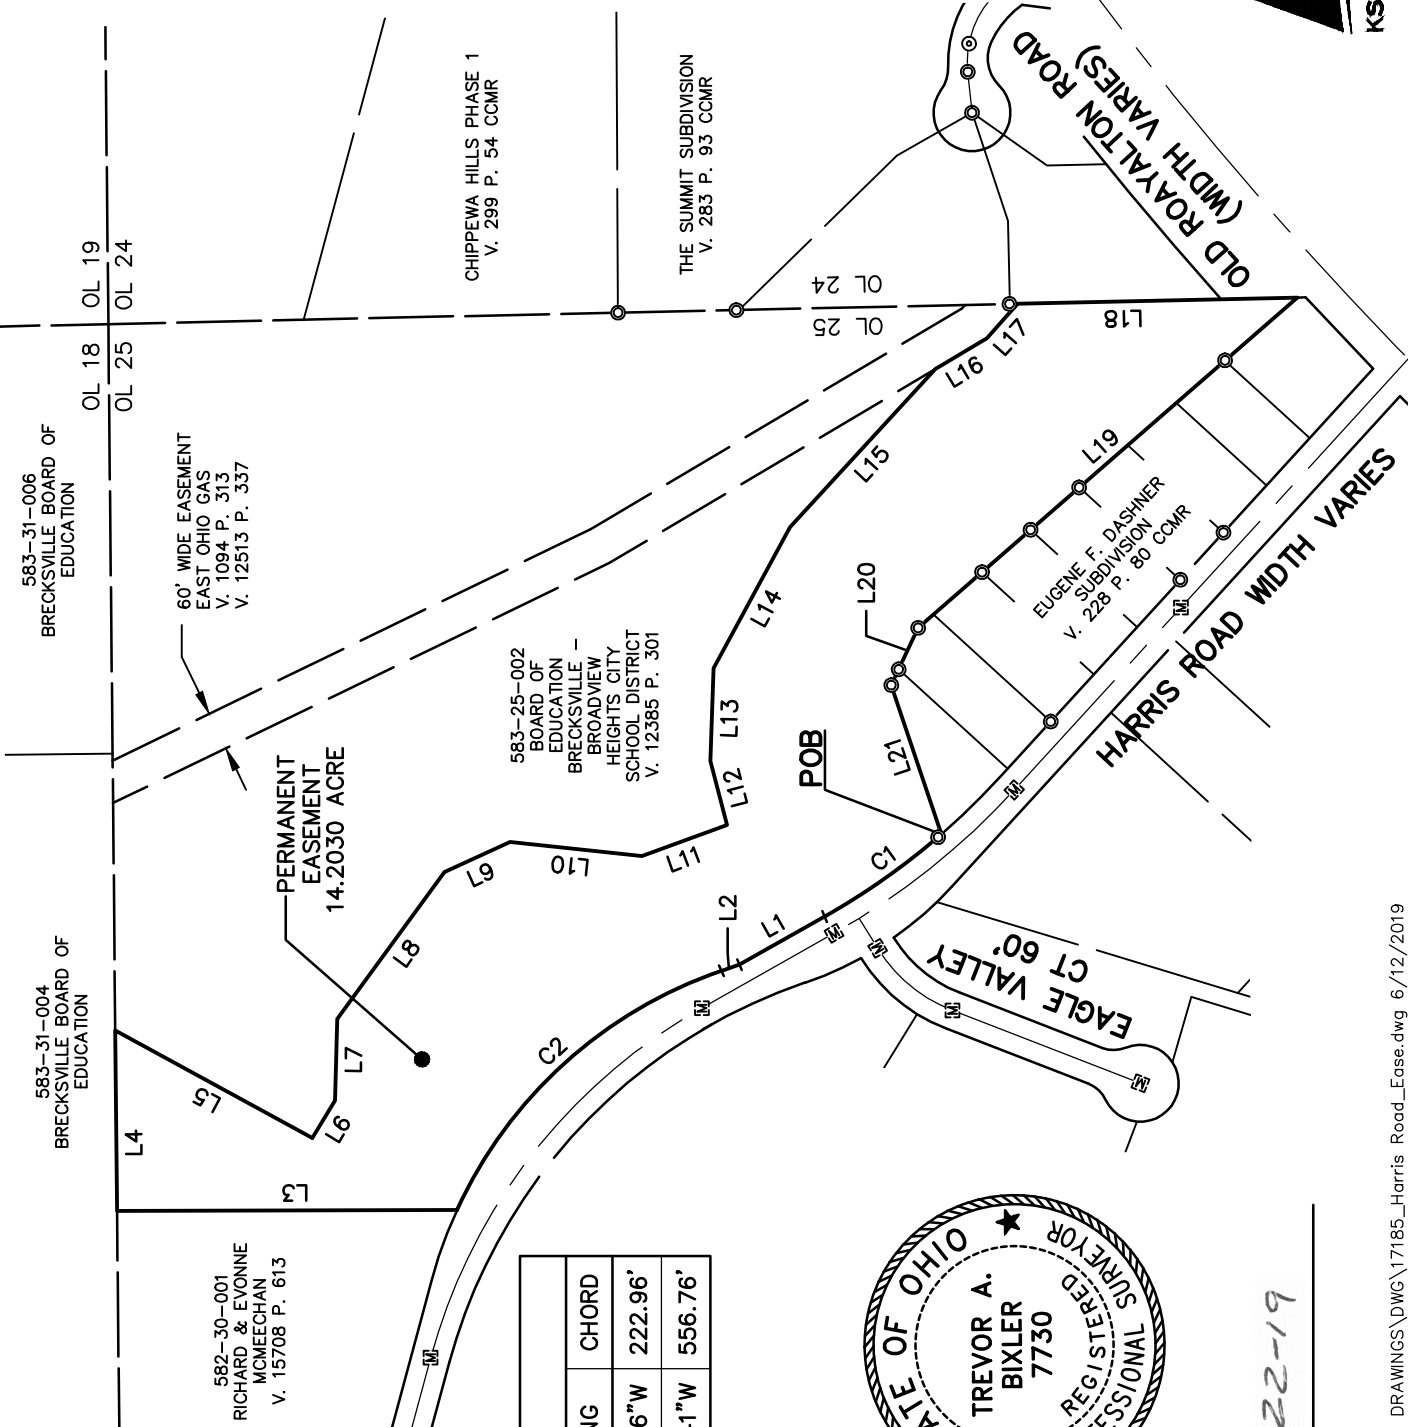

LINE TABLE		
LINE	BEARING	LENGTH
L1	N29°28'16"W	153.08'
L2	N18°52'14"W	29.66'
L3	N00°09'41"W	531.25'
L4	N89°26'10"E	281.59'
L5	S28°35'58"W	350.69'
L6	S58°44'02"E	68.42'
L7	S88°33'31"E	127.45'
L8	S53°50'19"E	284.29'
L9	S24°34'22"E	112.72'
L10	S06°00'27"W	206.76'
L11	S19°59'37"E	141.59'
L12	N75°20'55"E	103.19'
L13	S87°53'44"E	145.40'
L14	S61°32'12"E	250.35'
L15	S47°25'25"E	335.74'
L16	S30°44'34"E	93.25'
L17	S48°14'34"E	72.63'
L18	S01°16'48"E	436.94'
L19	N41°03'51"W	785.57'
L20	N64°49'15"W	98.80'
L21	S71°26'59"W	245.73'



KS Associates, Inc.
260 Burns Road, Suite 100
Elyria, OH 44035
P 440 365 4730
F 440 365 4790
www.ksassociates.com

KS ASSOCIATES

**Permanent Easement
Across PPN 583-25-002
14.2030 Acres
Page 1 of 2**

Situated in the City of Broadview Heights, County of Cuyahoga and State of Ohio, and known as being part of Original Brecksville Township Lot No. 25. Also being part of the land conveyed to Board of Education Brecksville – Broadview Heights City School District as recorded in Volume 12385, Page 301 of the Cuyahoga County Records, being more definitely described as follows:

Beginning in the easterly right of way of Harris Road (width varies) at the northwesterly corner of Eugene J. Dashner Subdivision as recorded in Volume 228, Page 80 of the Cuyahoga County Map Records;

Thence, along the easterly right of way of Harris Road the following four courses:

Along the arc of a curve which deflects to the right, 223.33 feet, said curve having a radius of 1115.92 feet, a central angle of 11° 28' 00", and a chord of 222.96 feet which bears North 35° 12' 16" West;

Thence, North 29° 28' 16" West, 153.08 feet;

Thence, North 18° 52' 14" West, 29.66 feet;

Thence, along the arc of a curve which deflects to the left, 572.34 feet to the easterly line of land conveyed to Richard and Evonne McMeechan as recorded in Volume 15708, Page 613 of the Cuyahoga County Records, said curve having a radius of 705.00 feet, a central angle of 46° 30' 53", and a chord of 556.76 feet which bears North 42° 07' 41" West;

Thence, leaving said easterly right of way along McMeechan's easterly line, North 00° 09' 41" West, 531.25 feet to the northerly line of said Original Brecksville Township Lot No. 25;

Thence, along the northerly line of said Original Brecksville Township Lot No. 25, North 89° 26' 10" East, 281.59 feet;

Thence, leaving said northerly line, South 28° 35' 58" West, 350.69 feet;

Thence, South 58° 44' 02" East, 68.42 feet;

Thence, South 88° 33' 31" East, 127.45 feet;

Thence, South 53° 50' 19" East, 284.29 feet;

Thence, South 24° 34' 22" East, 112.72 feet;

Thence, South 06° 00' 27" West, 206.76 feet;

Thence, South 19° 59' 37" East, 141.59 feet;

Thence, North 75° 20' 55" East, 103.19 feet;

Thence, South 87° 53' 44" East, 145.40 feet;

Thence, South 61° 32' 12" East, 250.35 feet;

**Permanent Easement
Across PPN 583-25-002
14.2030 Acres
Page 2 of 2**

Thence, South 47° 25' 25" East, 335.74 feet to the westerly line of a 60 foot wide easement to East Ohio Gas as recorded in Volume 1094, Page 313 and Volume 12513, Page 337 of the Cuyahoga County Records;

Thence, along the westerly line of said 60 foot wide easement the following two courses;

South 30° 44' 34" East, 93.25 feet;

Thence, South 48° 14' 34" East, 72.63 feet to the easterly line of said Original Brecksville Township Lot No. 25;

Thence, along the easterly line of said Original Brecksville Township Lot No. 25, South 01° 16' 48" East, 436.94 feet to the easterly line of said Eugene F. Dashner Subdivision;

Thence, leaving the easterly line of said Original Brecksville Township Lot No. 25 along the easterly line of said Eugene F. Dashner Subdivision the following three courses;

North 41° 03' 51" West, 785.57 feet;

Thence, North 64° 49' 15" West, 98.80 feet;

Thence, South 71° 26' 59" West, 245.73 feet to the point of beginning.

Containing within said bounds 14.2030 acres of land as surveyed by KS Associates, Inc. under the supervision of Trevor A. Bixler, Professional Surveyor, No. 7730 in April and May, 2019.

Bearings are based on the Ohio State Plane, North Zone, NAD83(2011) Grid North.

T. A. Bixler 5-22-19

Trevor A. Bixler, P.S.
Professional Surveyor, Ohio No. 7730

KS ASSOCIATES
Civil Engineers + Surveyors

260 Burns Road, Suite 100
Elyria, OH 44035
440 365 4730

